


流动之城 · 京张AI代谢创新带 —— 总体概念

一带（代谢主轴）· 三核（器官）· 两翼（赋能）· 多节点（循环）

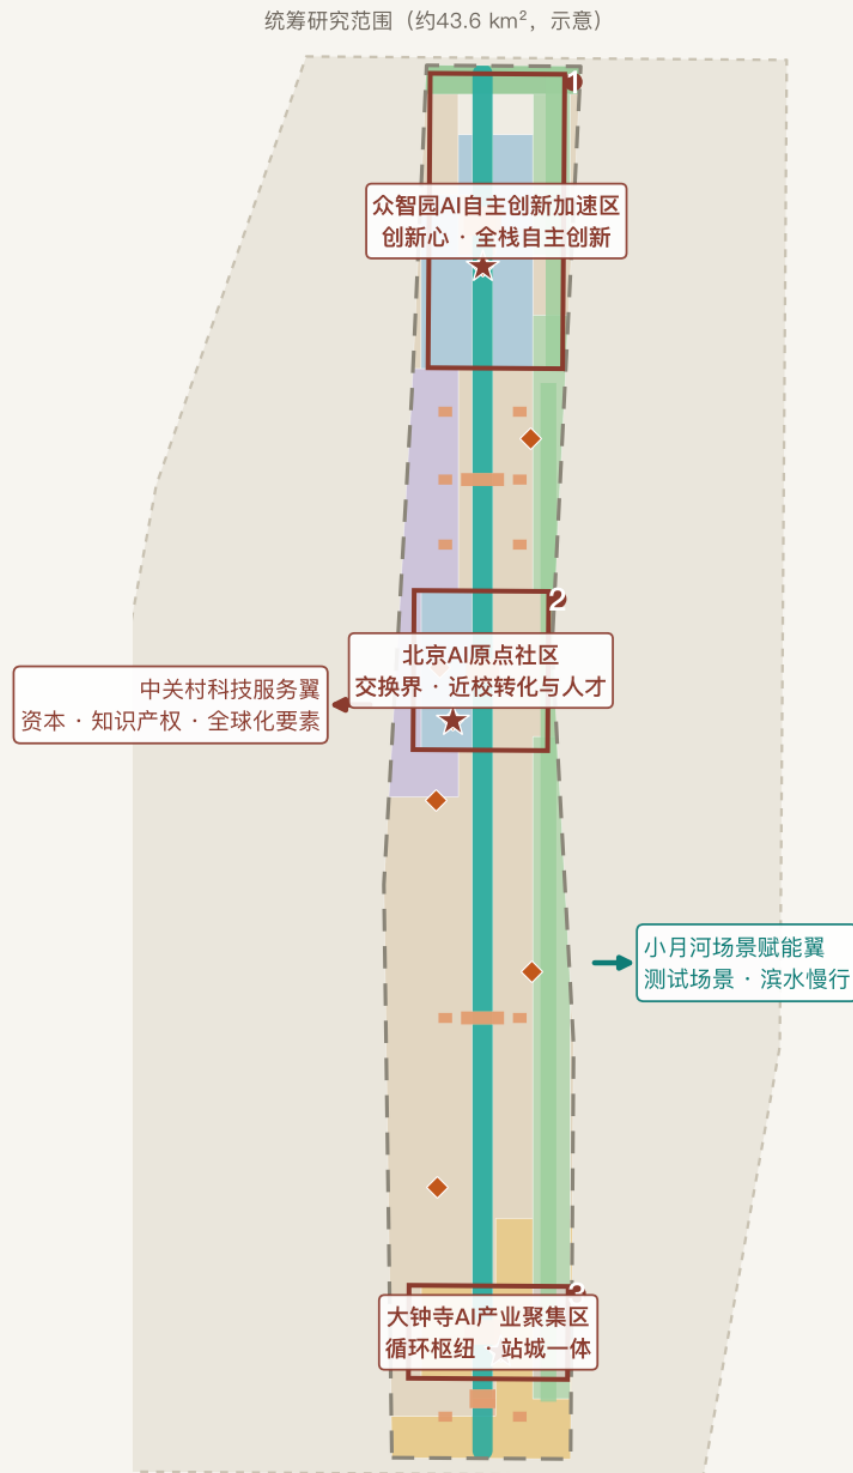

京张绿脊（代谢主轴）

- 京张绿脊（代谢主轴）
- 公共空间节点（广场/前院）
- 代谢节点（端侧算力驿站 + 场景接口，概念）
- AI朝圣地标（3处，概念）
- 重点区临时范围
- 临时边界

三核 · 三种器官角色

- 众智园AI自主创新加速区**
创新心 · 全栈自主创新
- 北京AI原点社区**
交换界 · 近校转化与人才
- 大钟寺AI产业聚集区**
循环枢纽 · 站城一体

总体设计范围
约 11.4 km²

临时粗略边界（provisional）——非官方红线，官方数据到位后整体复算

资料来源：仓库临时边界与公告文字四至；公告总体设计范围约11.4 km²；面积复算 EPSG:4548。概念建议，非法定规划。


设计依据与三层范围

公告为第一依据；临时边界仅用于生成与自检

- 依据：资格预审公告（三层范围、三处重点区、任务与深度）与智能体任务书。
- 边界：总体设计范围 PROV-SITE-001、重点区 PROV-KEY-001/002/003，均为临时粗略边界。
- 三层：43.6 km ² 统筹研究 → 11.4 km ² 总体设计 → 368.4 ha 重点区。
- 方法：先锁边界与约束，再生成图层，最后复算指标（EPSG:4548）。

流动之城 · 京张AI代谢创新带 —— 总体概念

一带（代谢主轴）· 三核（器官）· 两翼（赋能）· 多节点（循环）

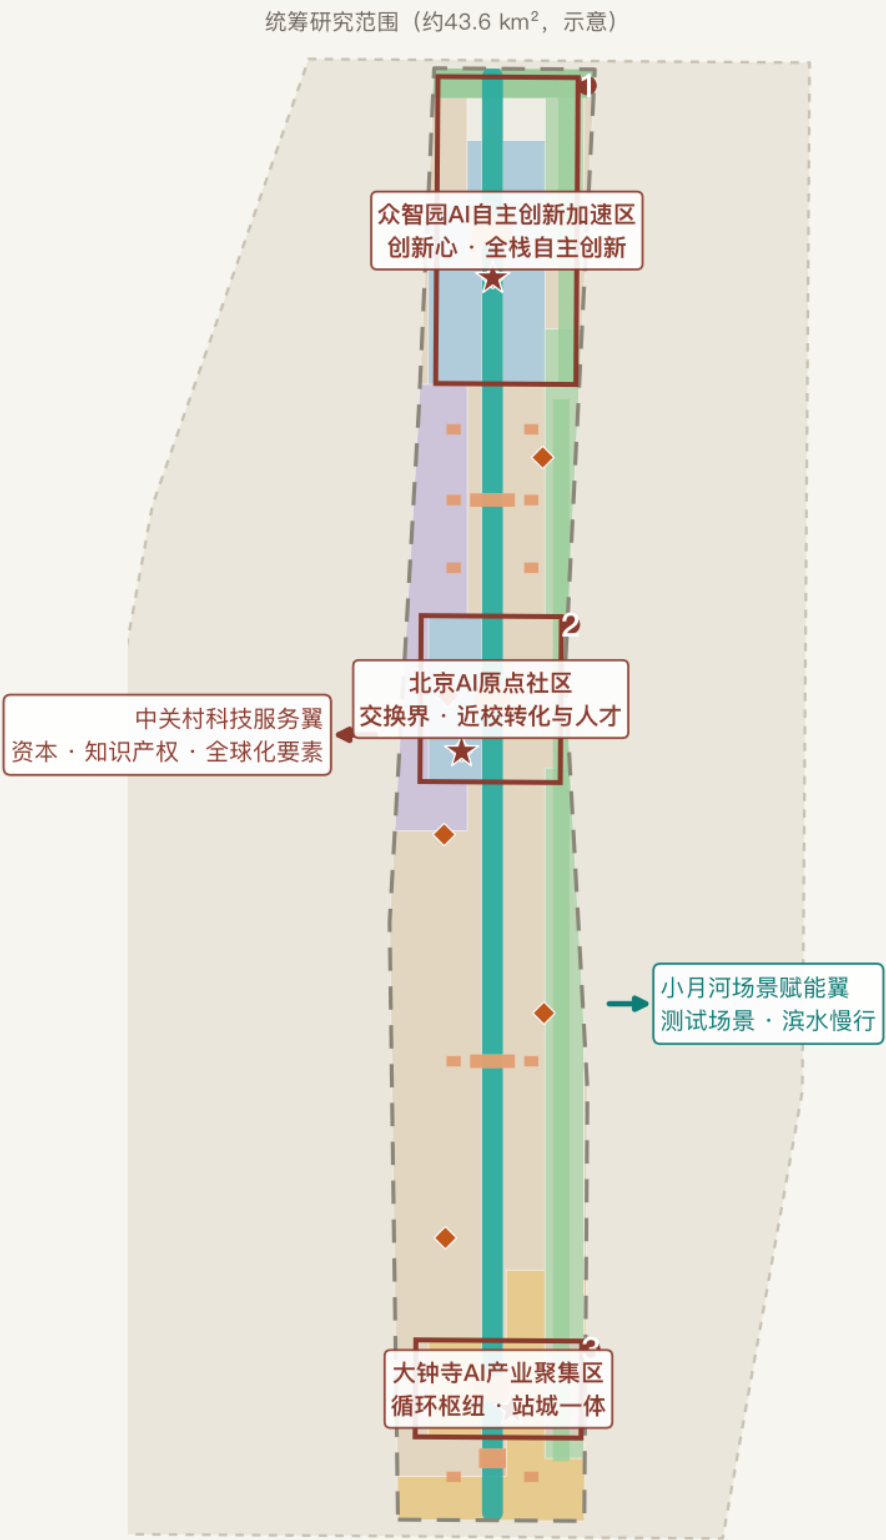

京张绿脊（代谢主轴）

- 京张绿脊（代谢主轴）
- 公共空间节点（广场/前院）
- 代谢节点（端侧算力驿站 + 场景接口，概念）
- AI朝圣地标（3处，概念）
- 重点区临时范围
- 临时边界

三核 · 三种器官角色

- 众智园AI自主创新加速区
创新心 · 全栈自主创新
- 北京AI原点社区
交换界 · 近校转化与人才
- 大钟寺AI产业聚集区
循环枢纽 · 站城一体



总体设计范围
约 11.4 km²

临时粗略边界（provisional）——非官方红线，官方数据到位后整体复算

资料来源：仓库临时边界与公告文字四至；公告总体设计范围约11.4 km²；面积复算 EPSG:4548。概念建议，非法定规划。

用地结构与空间组织

完整覆盖 · 无缝分区 · 国土空间用地代码；绿脊为代谢主轴

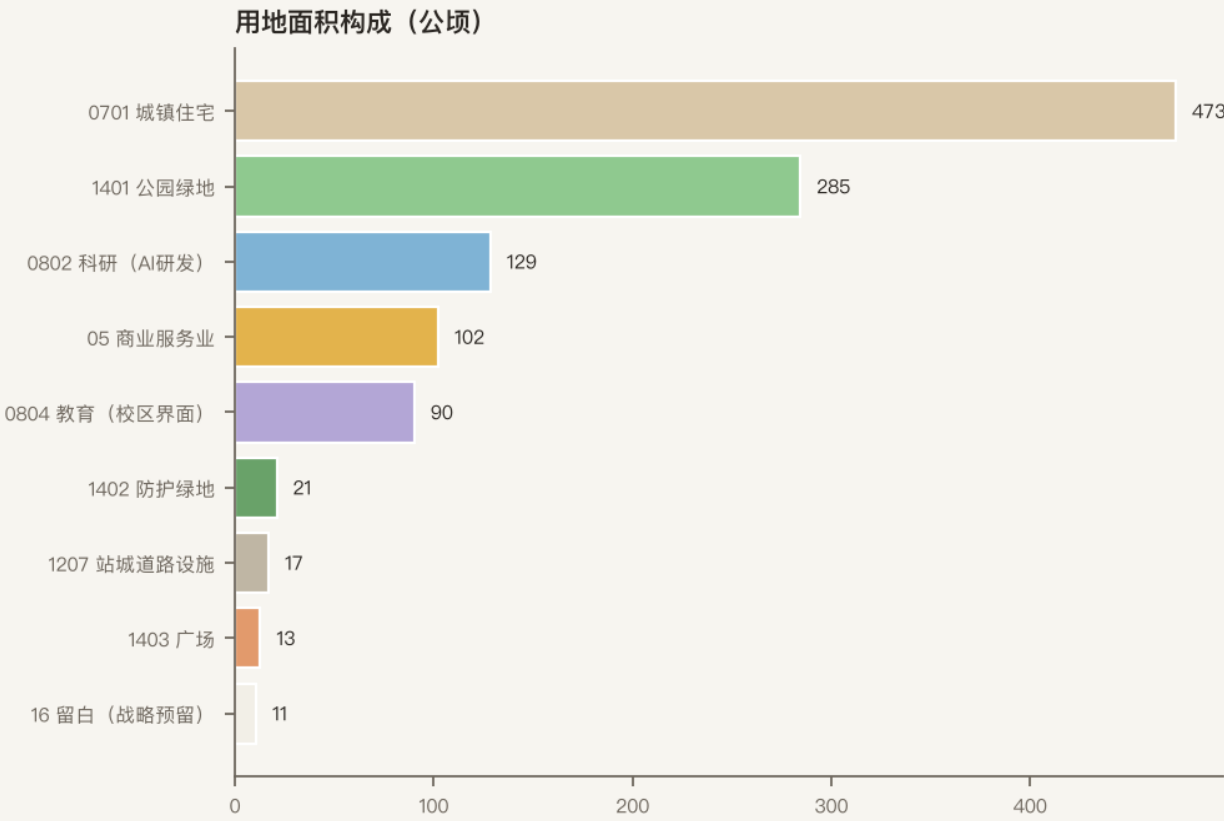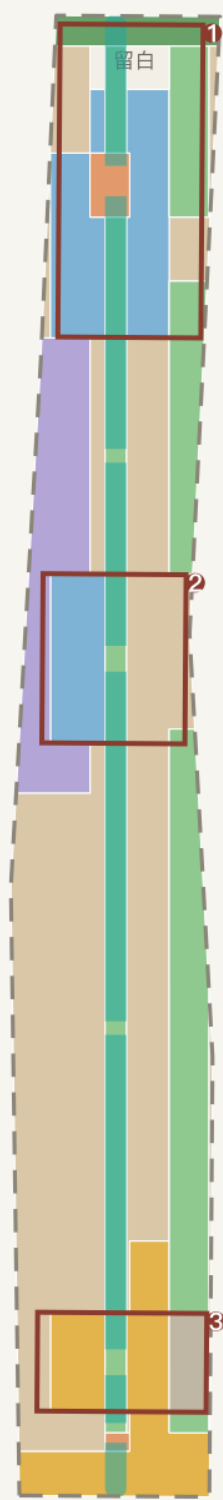


临时粗略边界（provisional）——非官方红线

资料来源：geometry/land_use.geojson（EPSG:4548 复算）；用地代码见场地包枚举。概念建议，非法定规划。

三处重点区域：三种器官角色

临时矩形占位（provisional）· 公告面积 · 定位—动作—场景

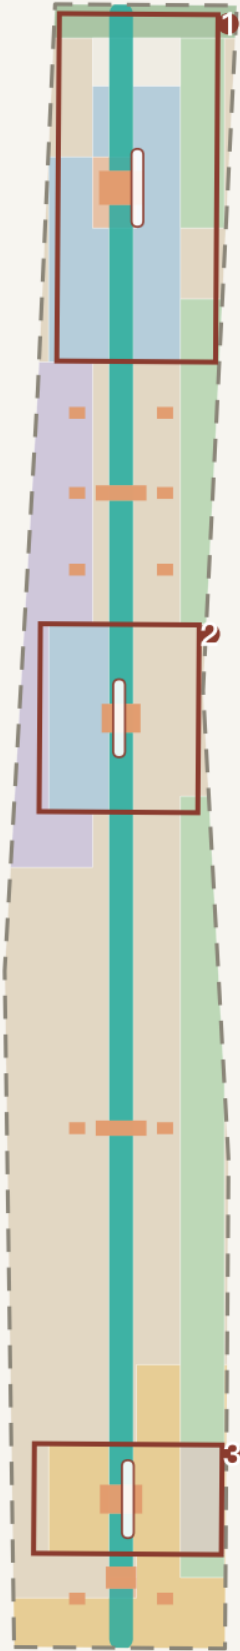

① 众智园AI自主创新加速区 · 创新心

公告约 192.1 ha

定位：花园式全栈自主创新加速区

动作：北端战略留白 | 研发组团与全栈实验集群 | 清河创新绿缘

场景：开放测试场 · 红队沙盒 · 标准工作坊 · 低碳算力体验

② 北京AI原点社区 · 交换界

公告约 104.3 ha

定位：近校成果转化与人才社区

动作：孵化街坊 + 人才公寓围绕发布广场 | 校区共享绿带缝合

场景：开源发布厅 · 转化Copilot服务街 · 适老服务站

③ 大钟寺AI产业聚集区 · 循环枢纽

公告约 72.0 ha

定位：站城一体智能经济与国际交往门户

动作：站前广场四象限连通 | 站城接驳综合体 | 商业组团更新


场景：国际路演客厅 · 数据要素展示窗 · AI夜间经济导航

重点区临时范围：公告未给四至，矩形仅承担生成与讨论占位，非地块或道路红线。

资料来源：geometry/key_areas.geojson 与公告面积；EPSG:4548。概念建议，非法定规划。

交通慢行与蓝绿公共空间复合系统


一脊 · 两道 · 七缝合 · 多接驳；蓝绿手指与广场网络

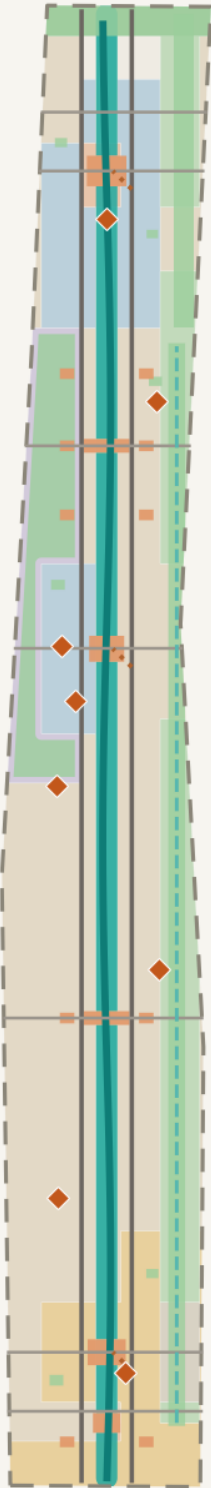

要素图例

- 绿脊慢行主脉
- 概念联络道
- 东西缝合支路
- 小月河骑行道
- 轨道接驳（概念）
- 京张绿脊
- 蓝绿手指
- 广场/前院
- 场景节点

绿脊典型剖面（概念示意）

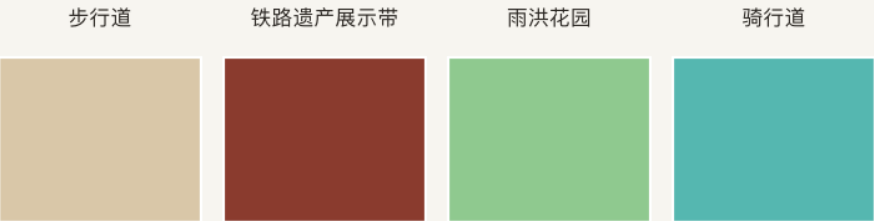

场景载体示例：SC-05 慢行陪伴 · SC-06 站城引导 · SC-11 雨洪感知

道路为概念中心线，非道路红线；轨道站点位置待官方确认。

资料来源：geometry/roads.geojson、green_space.geojson、public_space.geojson；EPSG:4548。概念建议，非法定规划。

AI 场景、画像与地标

12 场景卡 · 5 画像 · 3 地标

- 场景卡 12 张（含 4 张产业测试验证）：发布厅、测试场、红队沙盒、低速物流、慢行陪伴等。
- 画像 5 类：开发者、研究者、创始人、老年居民、国际访客；均含隐私边界与人工复核。
- 地标 3 处：天佑之舵、原点代码碑、流动之环；荣誉展示三层体系。

更新项目、分期与运营


三期实施 · 四季活动 · 开放运营

- 更新项目 6 项（JZ-01~06），均列依赖、风险与评估指标，不承诺投资与审批。
- 三期：近期 2026-28 大钟寺/南段绿脊；中期 2028-31 众智园/北段；长期 2031+ 两翼与留白。
- 运营：四季活动 + 周常开发者聚会；场景开放清单制闭环；国际传播转化路径。

指标复算与证据链

GeoJSON → EPSG:4548 复算 → metrics.json → 图件 / HTML / PDF

空间证据（绿地/公共空间/建筑基底/重点区）

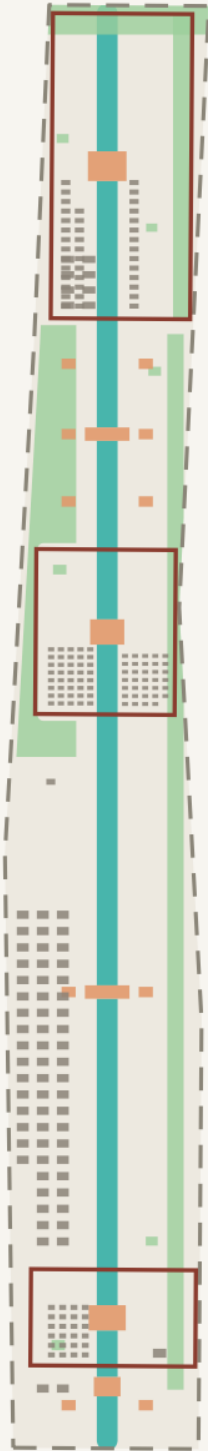

临时边界内指标仅用于生成与讨论；官方 polygon 到位后整体复算。
资料来源： geometry/* .geojson 与 metrics.json； EPSG:4548。概念建议，非法定规划。

已复算指标（known）

总体设计范围面积	11,412,825 m ² (约1141.3 ha)
绿地率（绿地/范围）	27.0%
公共空间占比	2.4%
建筑基底面积	499,602 m ²
建筑密度（概念基底）	4.4%
道路中心线总长（概念）	44,546 m
重点区数量	3
AI场景卡数量	12
用户画像数量	5
AI朝圣地标数量	3
全球案例数量	6
近期启动区面积	1,331,457 m ²

待正式数据补齐（unknown）

- 容积率 — 待正式控规条件
- 建筑高度控制 — 待正式控规条件
- 道路面积 — 待道路红线
- 总建筑面积 — 待容积率与边界

自检状态

- 确定性校验 PASS
- 空间复核 PASS
- 视觉封装 PASS
- 专业证据 PASS

风险、版权与合规

缺资料清单 · 双语 · 版权

- 缺资料：官方红线、控规、道路红线、权属、市政、文保、公共服务标准 —— 均待正式数据补齐。
- 替换规则：官方 polygon 到位后全图层、指标、图件、PDF、HTML 整体复算。
- 版权：图件与 PDF 由本包 GeoJSON/metrics 派生，无未清权素材；双语成对提供。
- 边界：不声称官方批准、审定控规、最终权属或保证实施。